

Planta de Coberturas



Piso 1 (térreo)





Cave

Assinado por: **Jorge Miguel Magalhães Alves**
Num. de Identificação: 13587360
Data: 2026.03.31 10:46:05 +0100

CHAVE MÓVEL


Os Gambozinos - Associação Cultural			
Pedido de Informação Prévia paro obras de Alteração Rua dos Castelos 135 Porto		Data: 03/2026 Ref: 2025-PJ05	01
Planta do Existente		Subs.:	Esc.: 1/100
Jorge Magalhães Alves, arquiteto	jorgemagalhaesalves@gmail.com		
AMA atelier, Rua de S. Dinis 556. 4250 - 428 Porto		tel.: + 351 918 800 122	

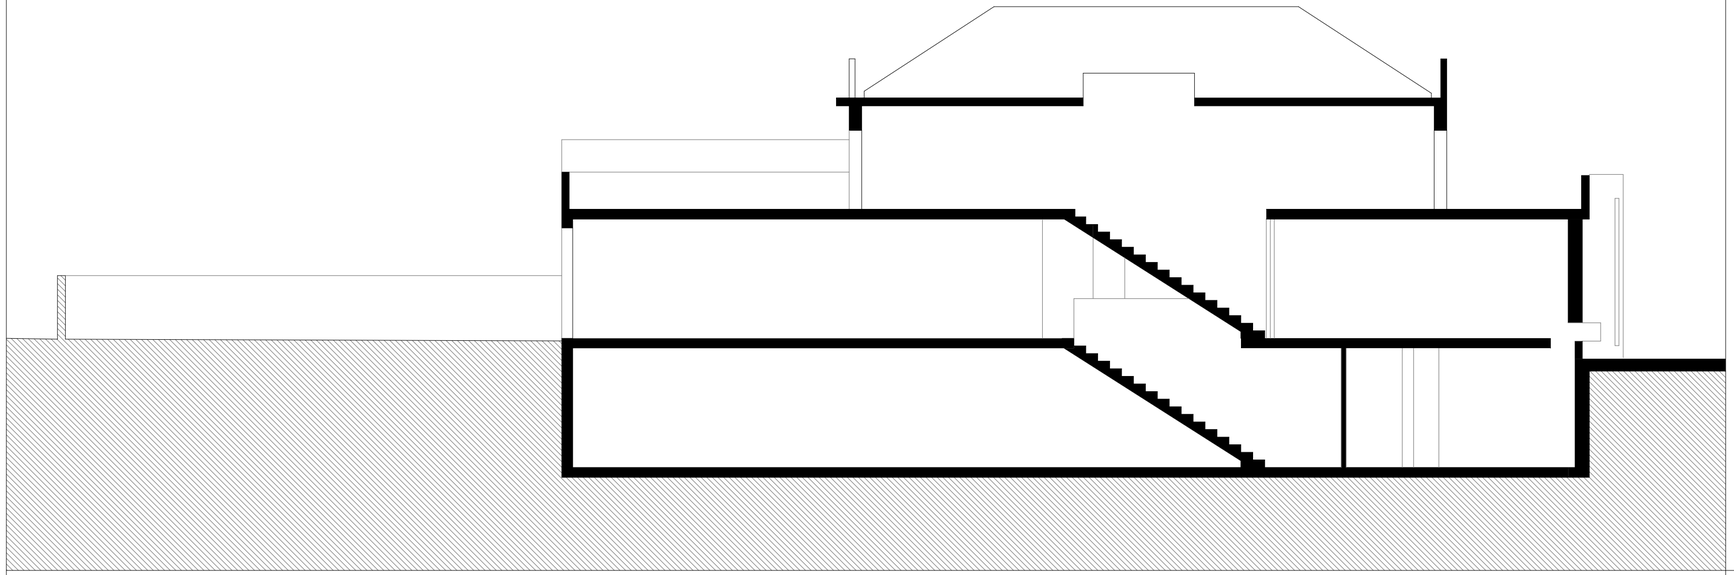

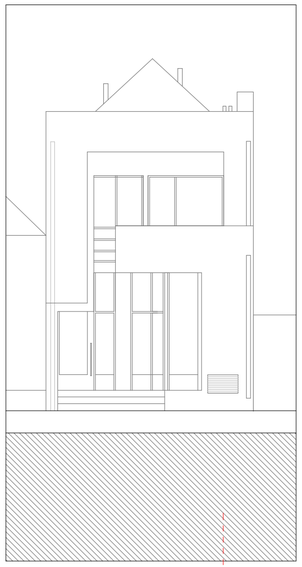


Os Gambozinos - Associação Cultural


Pedido de Informação Prévia paro obras de Alteração Rua dos Castelos 135 Porto	Data: 03/2026 Ref: 2025-PJ05	02
Corte A e Alçado Frontal Existente	Subs.:	Esc.: 1/100
Jorge Magalhães Alves, arquiteto jorgemagalhaesalves@gmail.com		
AMA atelier, Rua de S. Dinis 556. 4250 - 428 Porto	tel.: + 351 918 800 122	

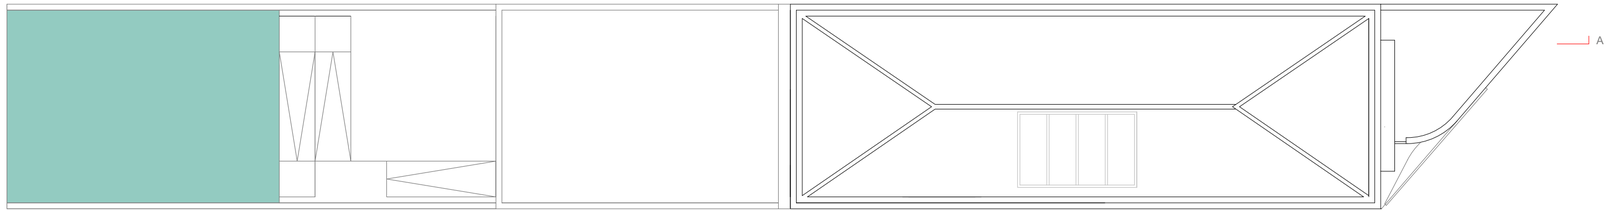

Planta de Coberturas

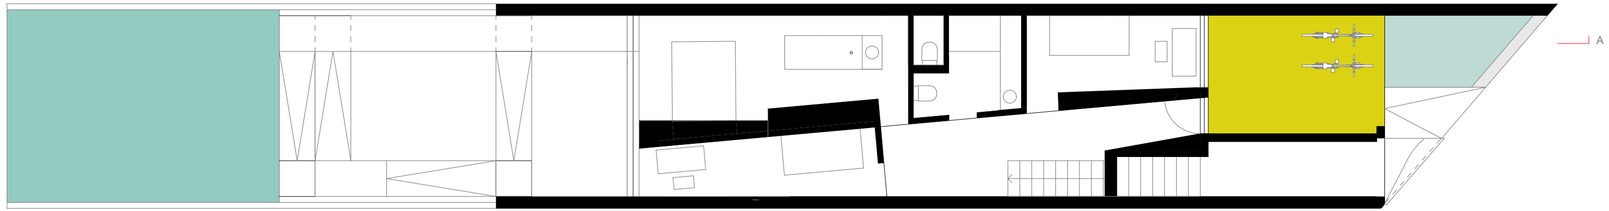

Piso 1 (térreo)

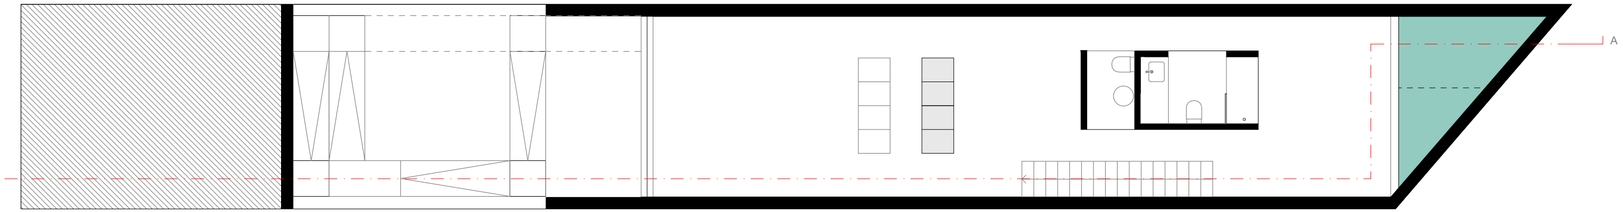

Cave

Os Gambozinos - Associação Cultural

Pedido de Informação Prévia paro obras de Alteração
Rua dos Castelos 135
Porto

Data: 07/2025

Ref: 2025-PJ05

03

Plantas da Proposta


Subs.:

Esc.: 1/100


Jorge Magalhães Alves, arquiteto jorgemagalhaesalves@gmail.com

AMA atelier, Rua de S. Dinis 556. 4250 - 428 Porto

tel.: + 351 918 800 122

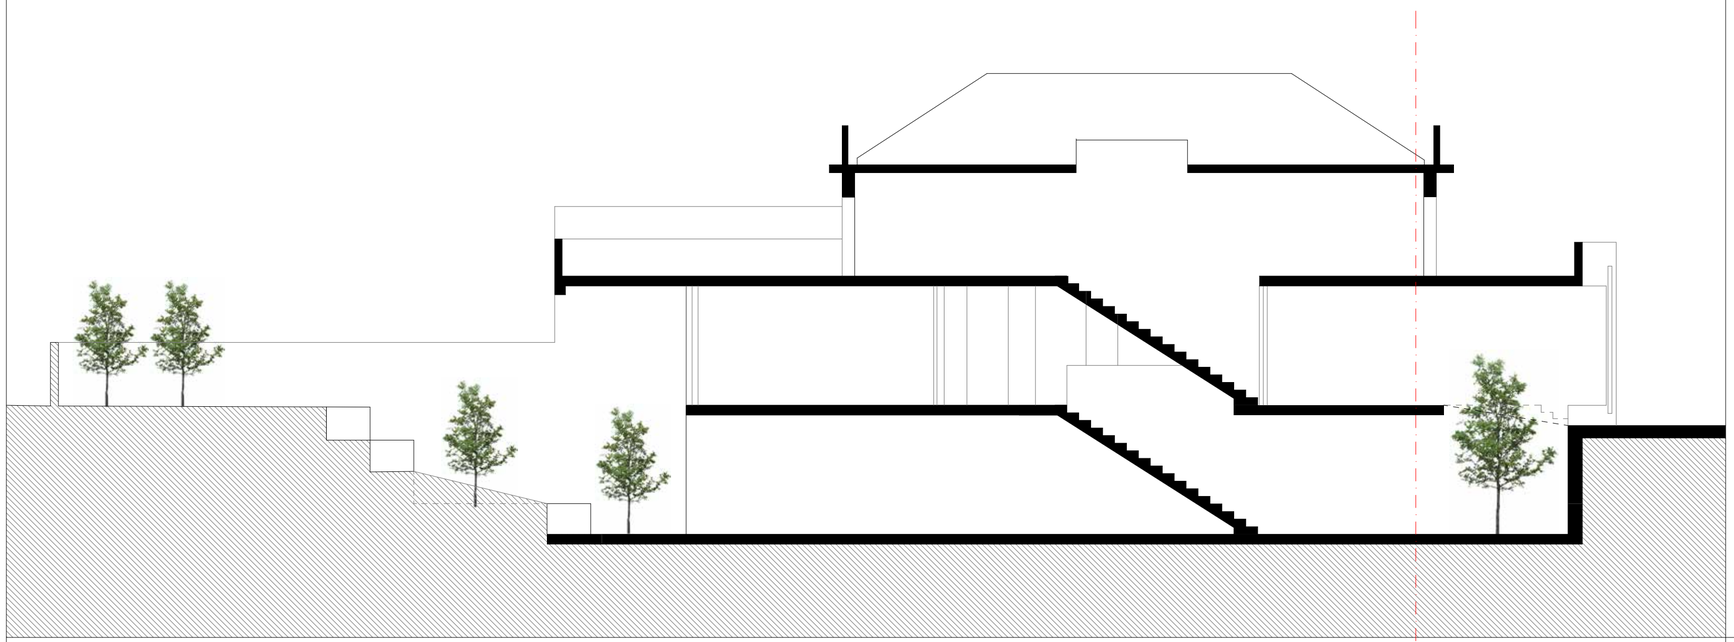


Corte A

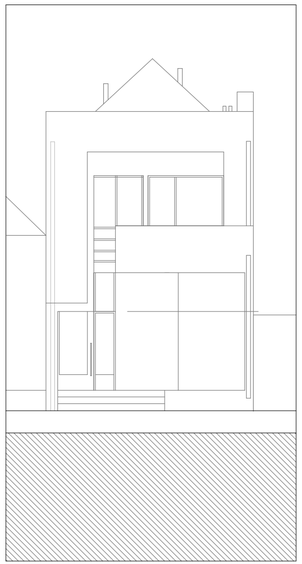


Os Gambozinos - Associação Cultural


Pedido de Informação Prévia paro obras de Alteração Rua dos Castelos 135 Porto	Data: 07/2025 Ref: 2025-PJ05	04
Corte A e Alçado Frontal da Proposta	Subs.:	Esc.: 1/100
Jorge Magalhães Alves, arquiteto jorgemagalhaesalves@gmail.com		
AMA atelier, Rua de S. Dinis 556. 4250 - 428 Porto	tel.: + 351 918 800 122	

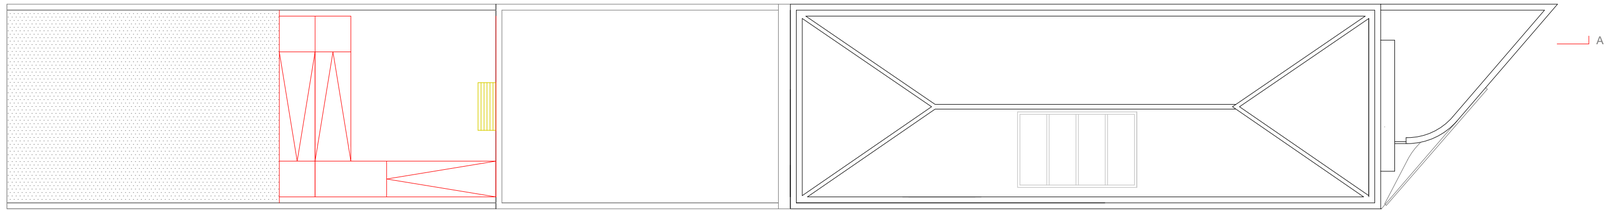

Planta de Coberturas

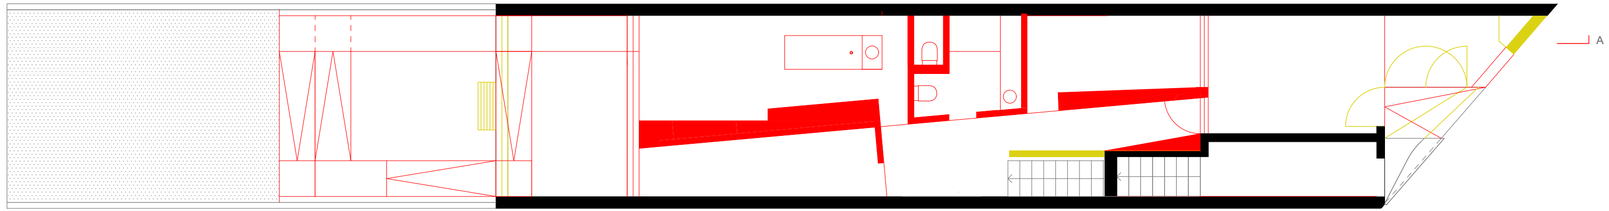

Piso 1 (térreo)

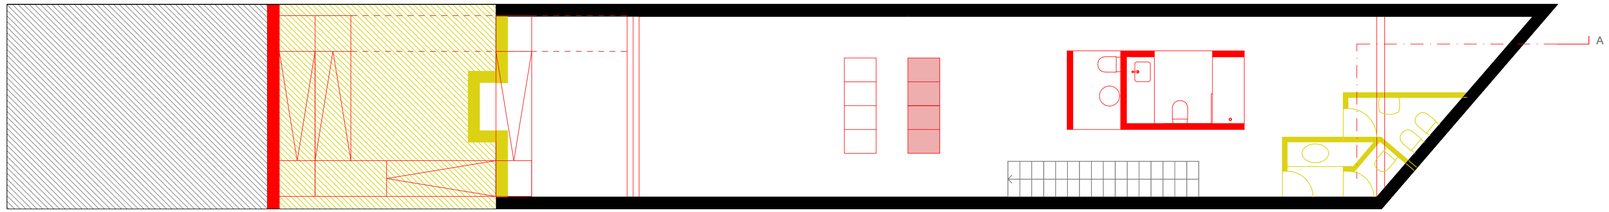

Piso -1

Os Gambozinos - Associação Cultural

Pedido de Informação Prévia paro obras de Alteração
Rua dos Castelos 135
Porto

Data: 03/2026

Ref: 2025-PJ05

05

Planta do Existente


Subs.:

Esc.: 1/100

Jorge Magalhães Alves, arquiteto jorgemagalhaesalves@gmail.com

AMA atelier, Rua de S. Dinis 556. 4250 - 428 Porto

tel.: + 351 918 800 122

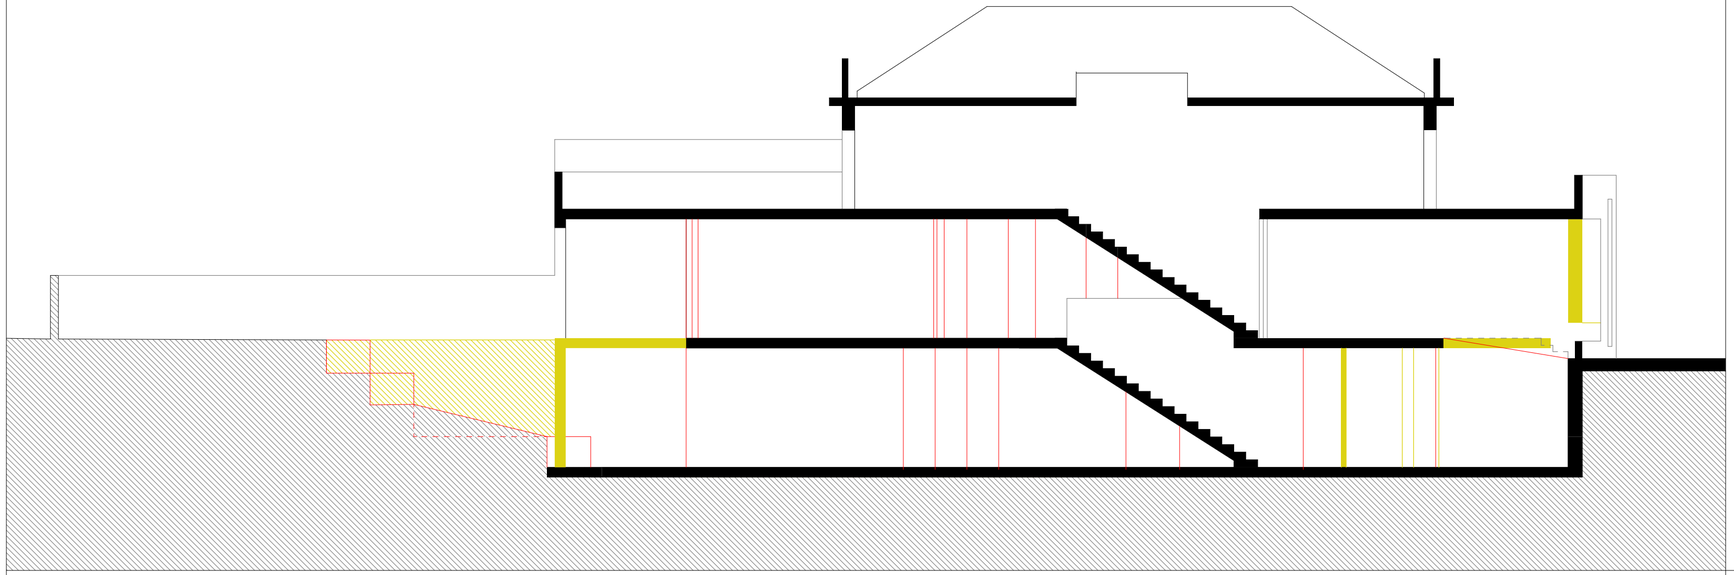



Os Gambozinos - Associação Cultural

Pedido de Informação Prévia paro obras de Alteração Rua dos Castelos 135 Porto	Data: 07/2025 Ref: 2025-PJ05	06
Corte A e Alçado Frontal Existente	Subs.:	Esc.: 1/100
Jorge Magalhães Alves, arquiteto jorgemagalhaesalves@gmail.com		
AMA atelier, Rua de S. Dinis 556. 4250 - 428 Porto	tel.: + 351 918 800 122	